


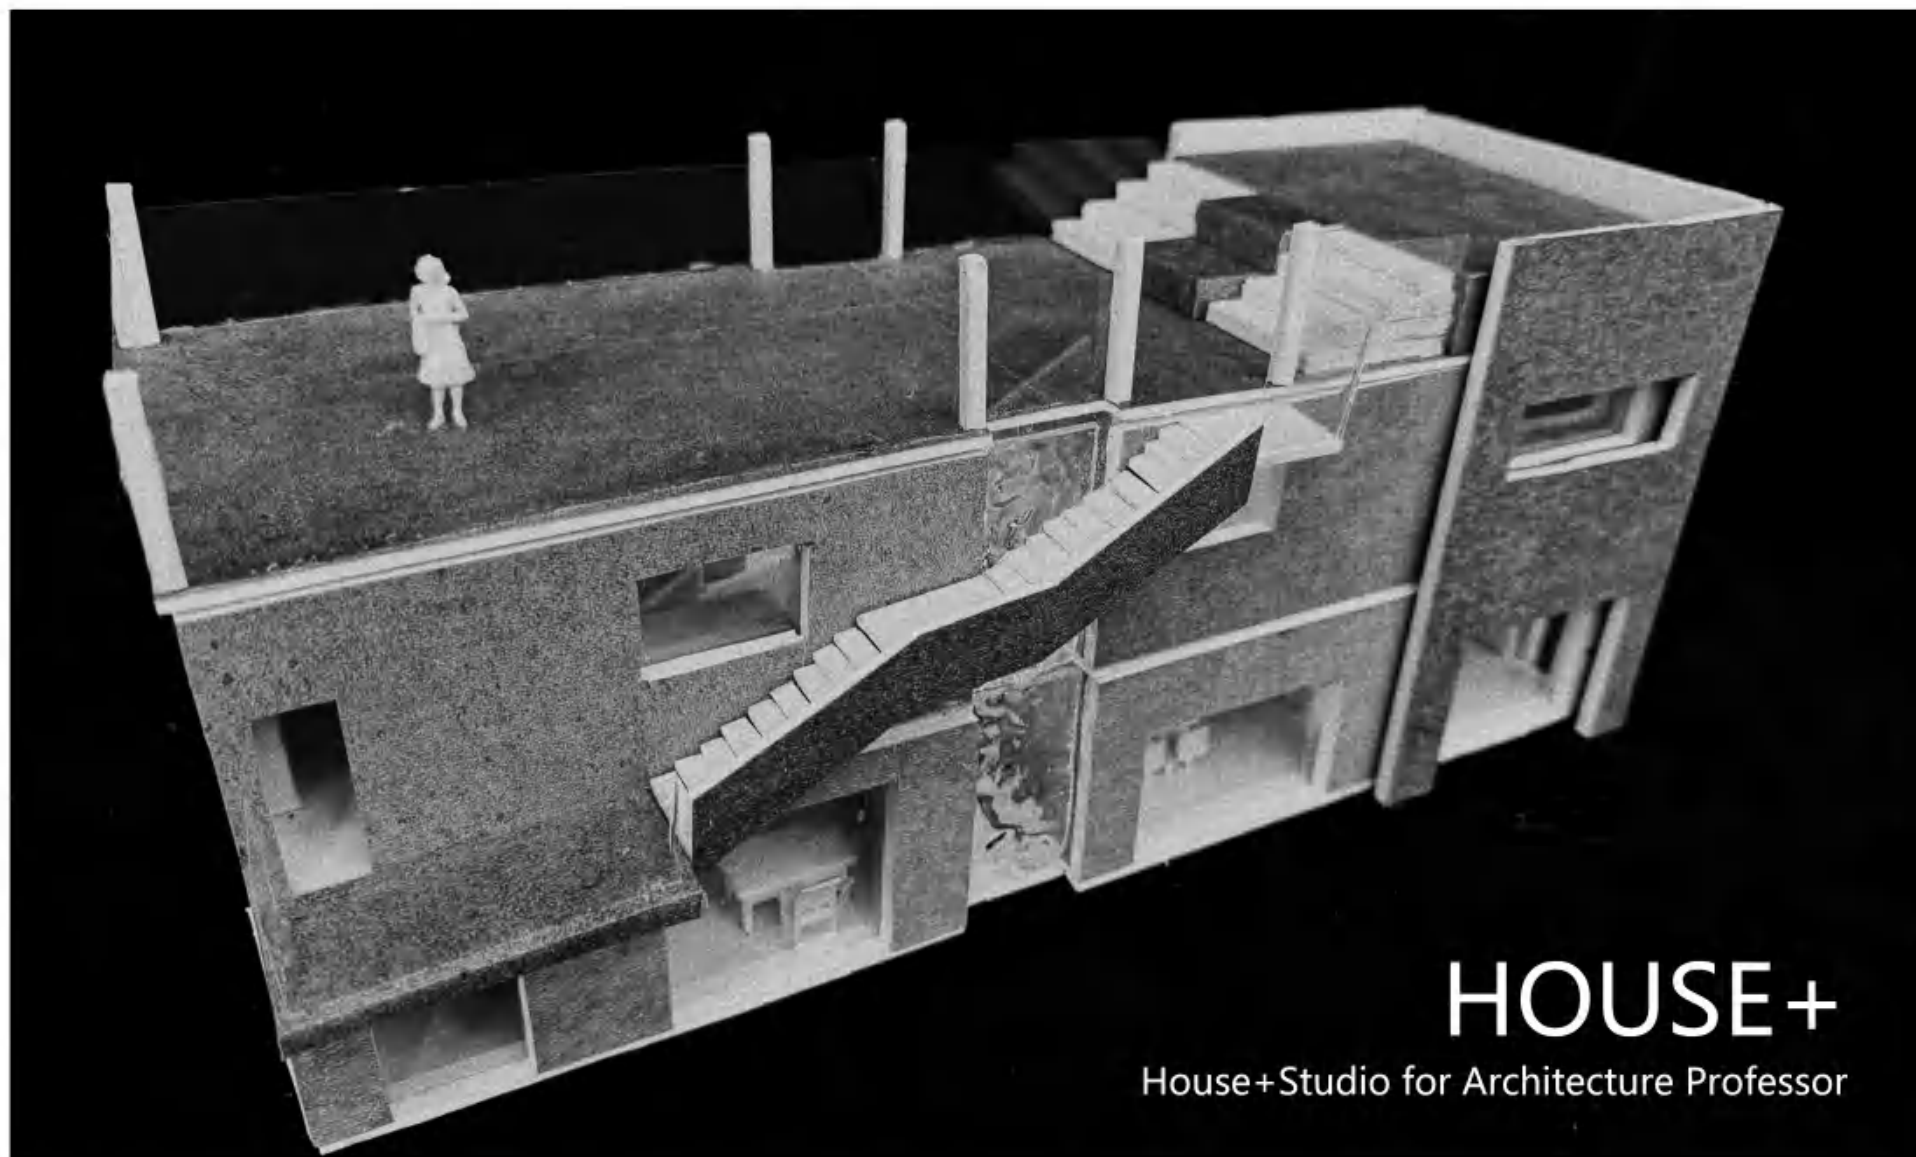

Client and Brief



Husband
Professor-Architecture

- | A quiet workspace
- | A reception area
- | Place for model display



Daughter
Student

- | Like to match clothes
- | An independent bedroom and a desk



Wife
Sculptor


- | A large space for sculpture making
- | Shelves for displaying materials
- | A rooftop for showcasing works



Son
Student


- | Like playing with Lego bricks
- | Independent bedroom

Site Analysis

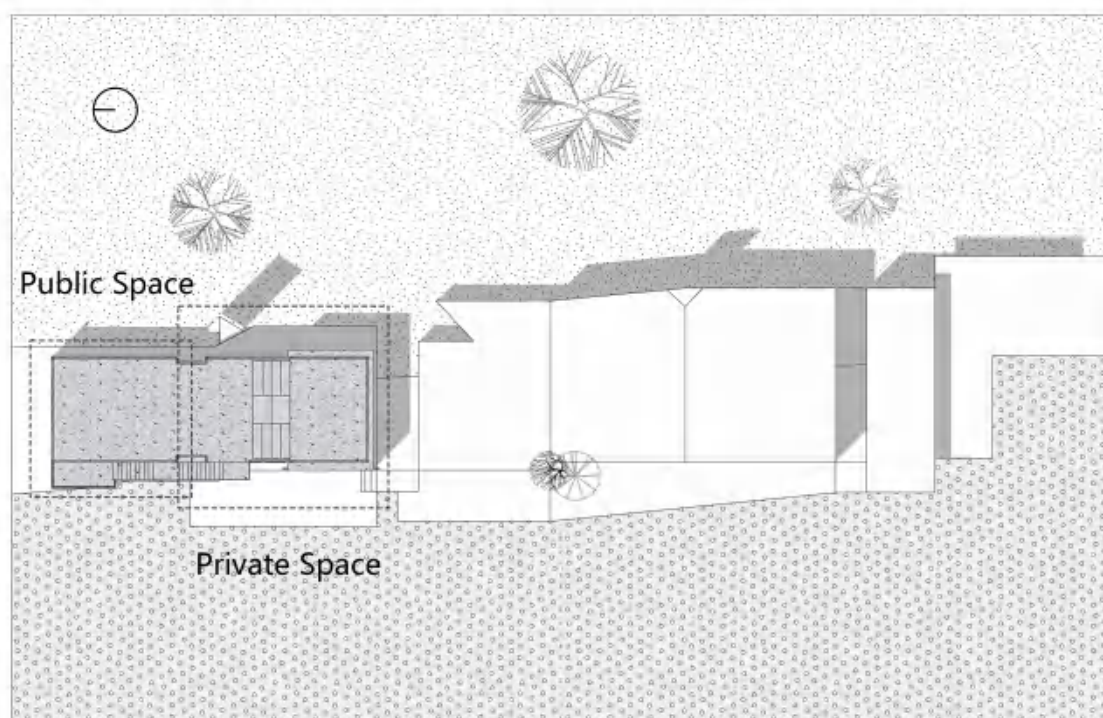


Site Plan 1:200

Explosive View

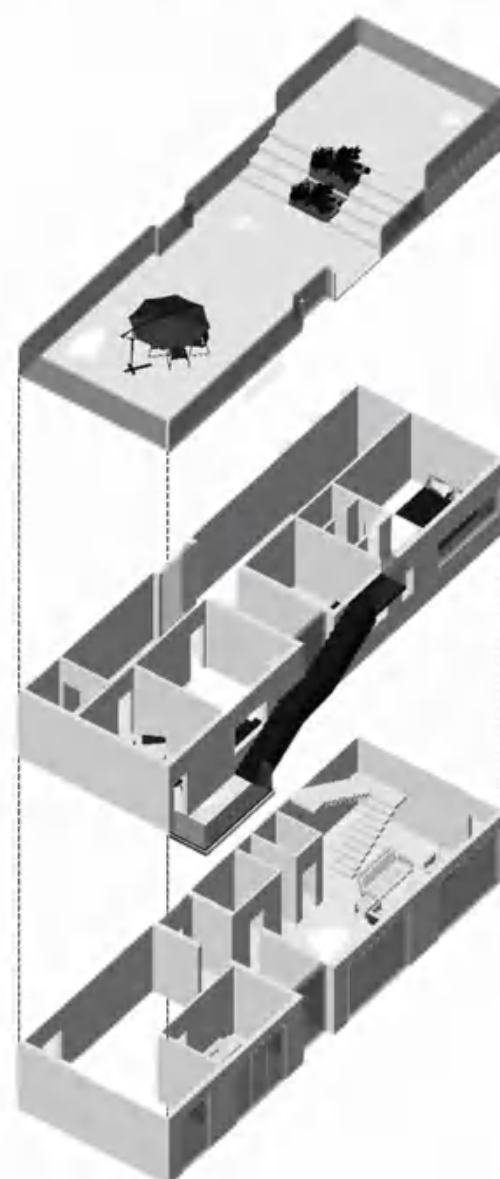


This residential studio design is based on the client's 'artistic needs', creating clear distinctions between work and living spaces, as well as public and private areas.

Architectural Drawings

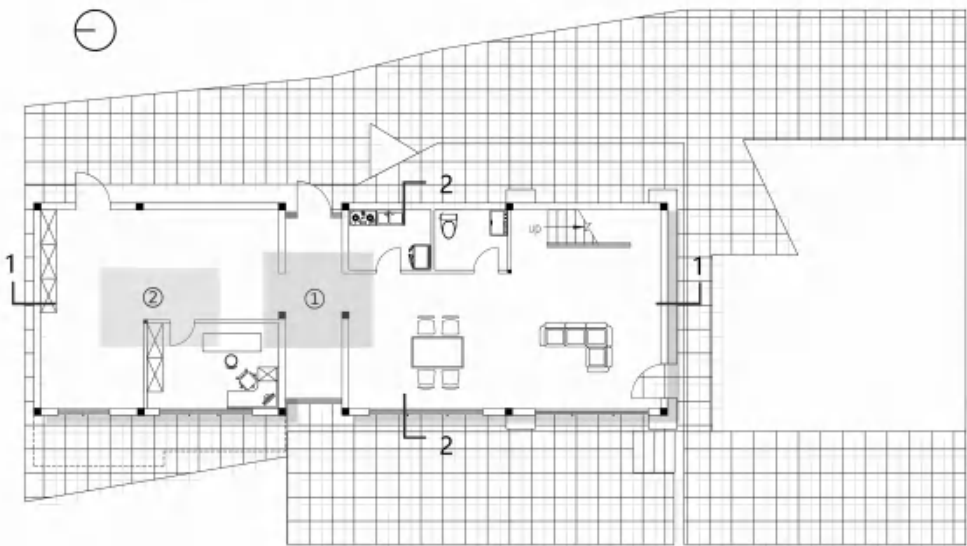

Ground Floor Plan 1:100

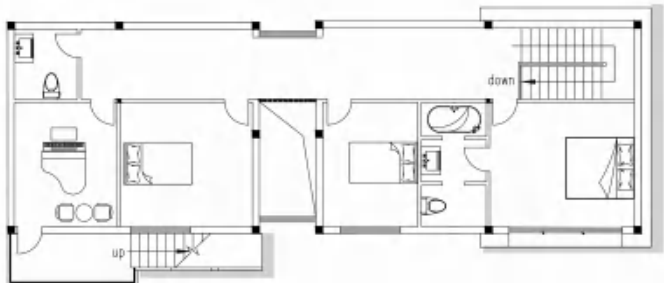


First Floor Plan 1:100




Second Floor Plan 1:100



Facade Material

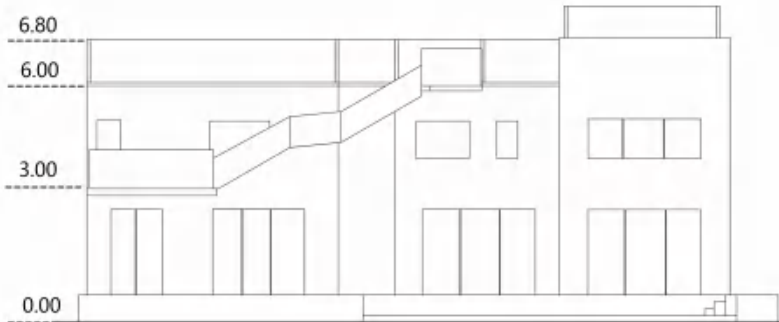

West Elevation 1:100

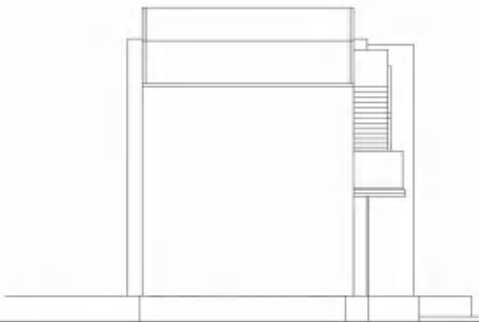

North Elevation 1:100



1-1 Section 1:100



2-2 Section 1:100

①
The hollow corridor design connecting the ground and first floors is used to link the work area with the living area.



At the same time, use frosted glass to achieve a beautiful light and shadow effect.

②
Large workspace for sculpture making and receiving guests.

